



上海永邺建筑工程设计咨询有限公司
ShangHai YongYe Construction Engineering Design Co.,Ltd

注意事项
BE CAREFUL

1. 本图纸所有尺寸以毫米为单位，切勿以比例量度此图，一切应依图内数字所示为准；
2. 图纸尺寸如与现场实际尺寸有所出入，所有尺寸需作实地复核，以现场放样为准；
3. 使用此图时，应同时参照其他建筑、结构及其他相关专业图纸，如发现有任何矛盾之处，应立即反馈设计单位；
4. 所有设计、图纸及设计说明版权权属上海永邺设计公司，非得到本公司书面同意，不得使用、抄袭或复制，如有发现必追究法律责任。

建设单位

上海虹元园林建设发展有限公司

业主确认 CONFIRM


项目负责人 P.M.		比例 SCALE	1:70
审核人 VERI.		阶段 PHASE	
校对 CK.		日期 DATE	
设计/制图 DESIGN/DRAW		版本 REV	

项目名称
PROJECT
新市北路1505号
办公用房室内装饰工程

图纸名称
DRAWING NAME
二层平面布置图

工程编号
CONSTRUCTION NUMBER
2020HK-02

图号
SHT. NO.
2P-01

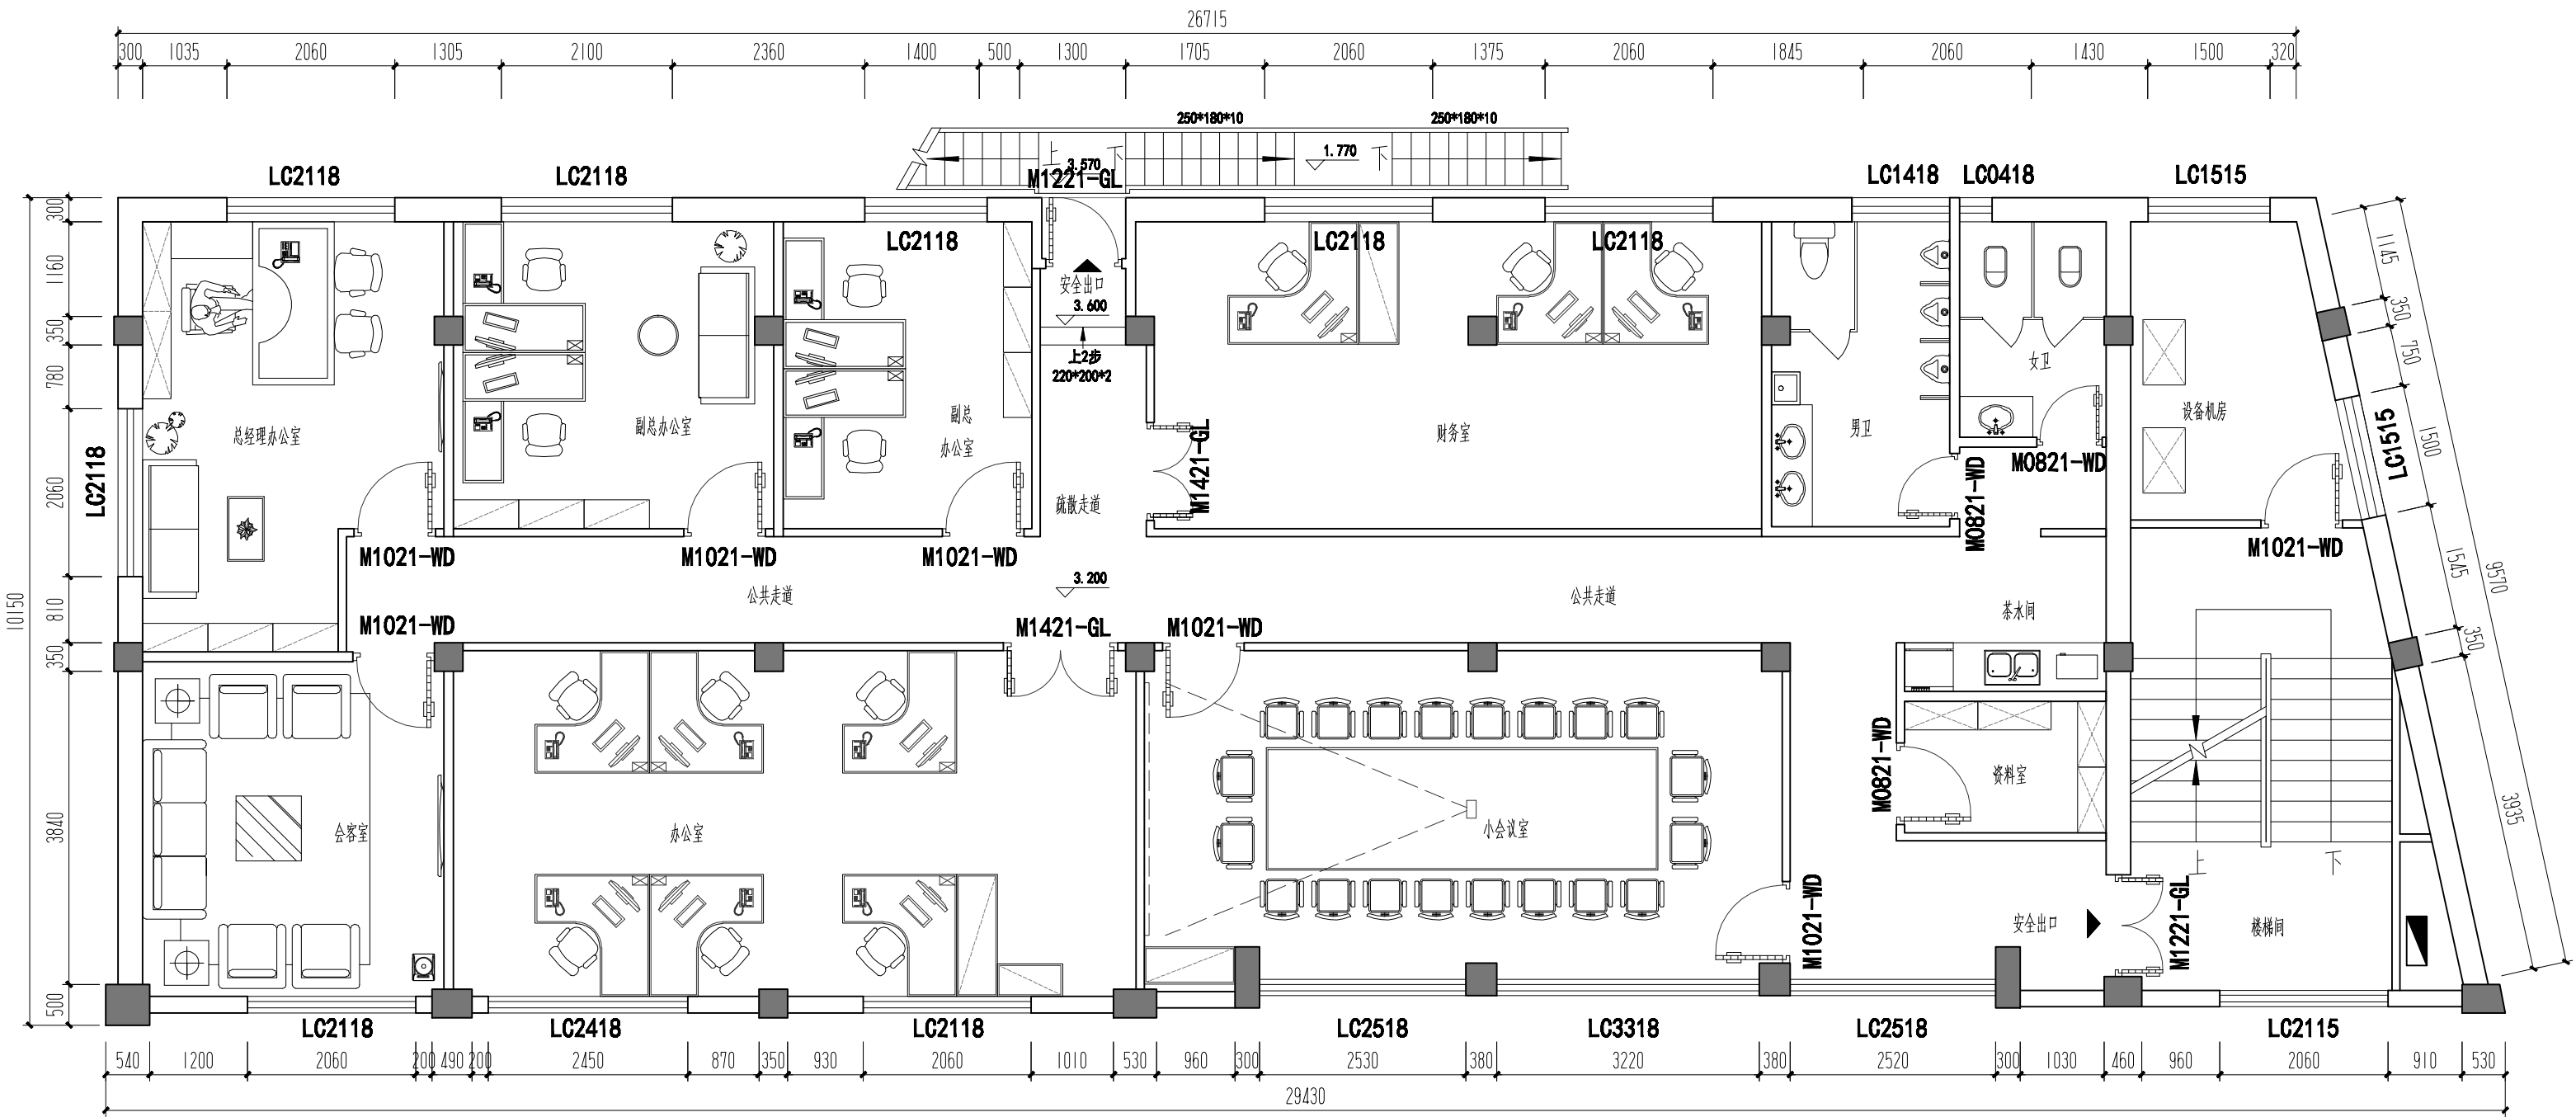

注：图上尺寸仅供参考，以现场实际尺寸为准

二层平面布置图